


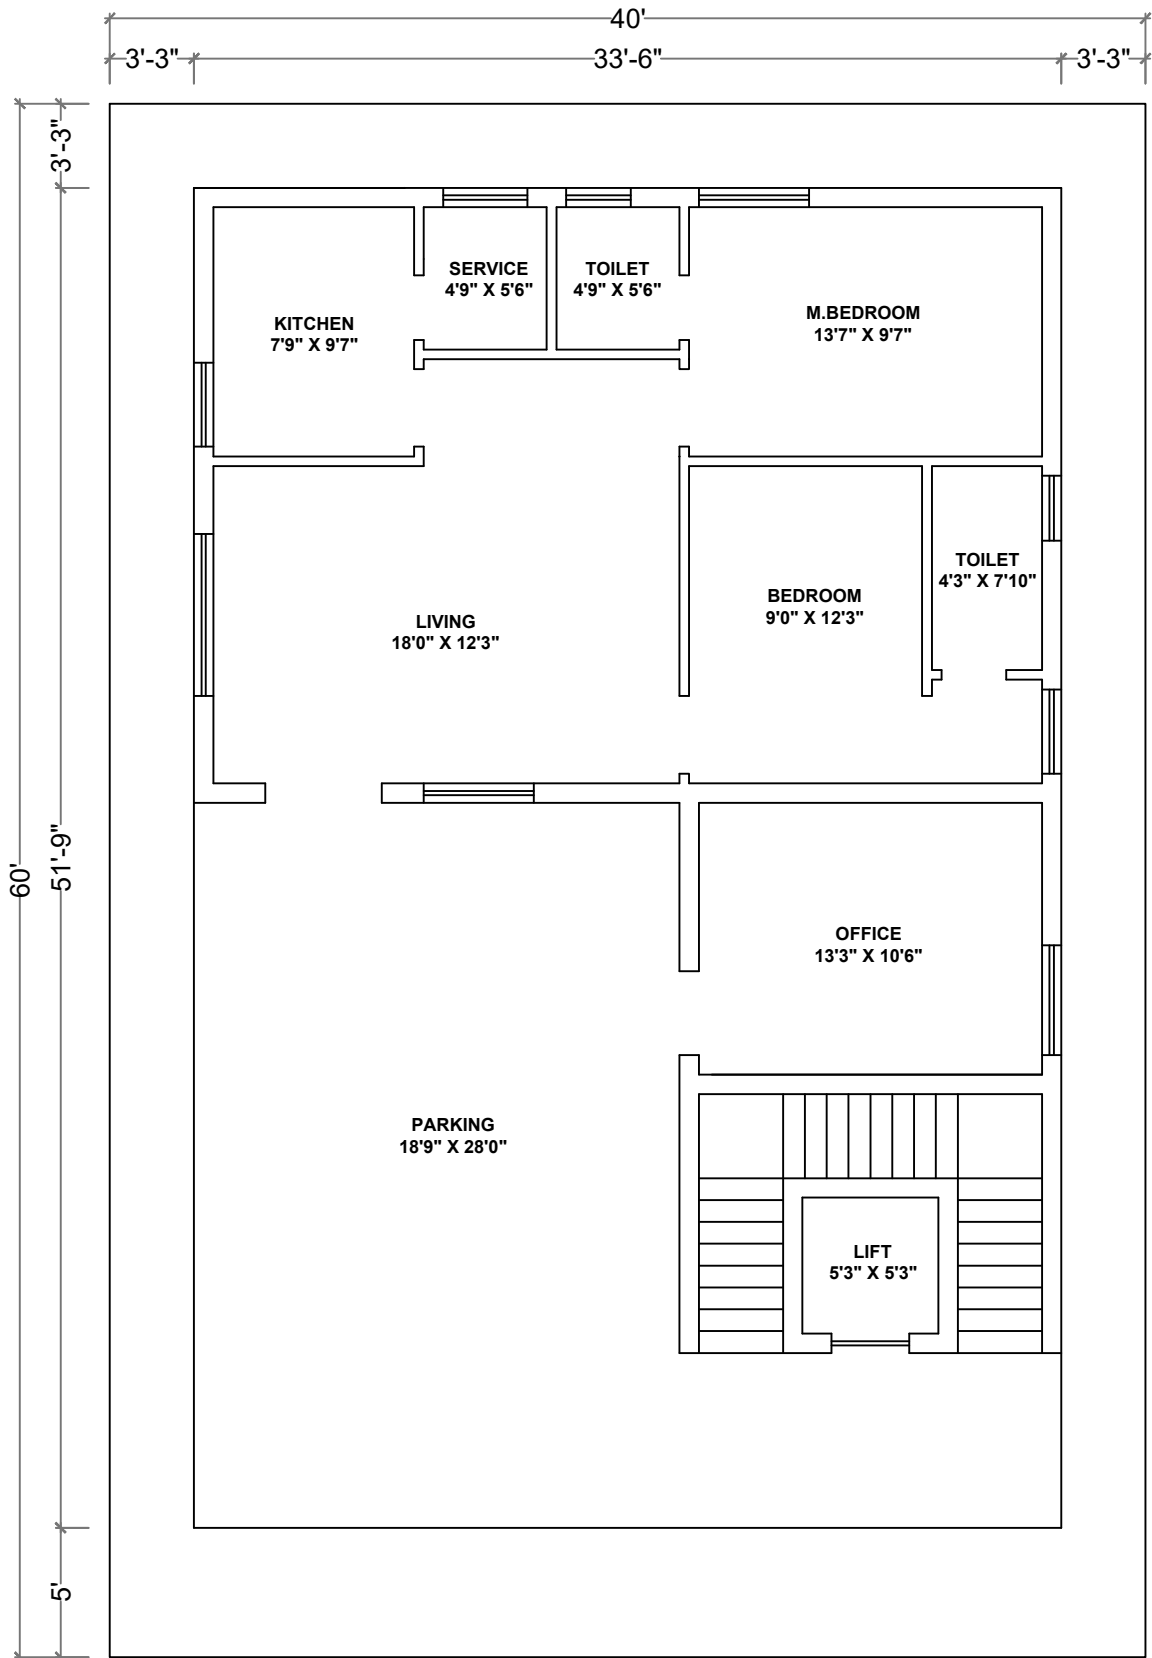

NOTES:

1. ALL THE DIMENSIONS MENTIONED ARE IN FEET & INCHES.
2. DRAWINGS NOT TO BE SCALED ONLY WRITTEN DIMENSIONS TO BE FOLLOWED.
3. ANY DISCREPANCIES FOUND IN THE DRAWING SHALL BE BROUGHT TO THE NOTICE OF THE CONSULTANT BEFORE EXECUTION.
4. RELEVANT SERVICES DRAWING TO BE READ SIMULTANEOUSLY.
5. FINISHED FLOOR TO BE 100MM FROM UNFINISHED FLOOR LEVELS.

ORIENTATION:



CLIENT NAME:

SRI.D.VENKATA RAO
 CHECKED BY: SYAM APPROVED BY: SESHAREDDY DATE: 10-02-2026

TITLE:

GROUND FLOOR PLAN

PROJECT NAME:
 RESIDENTIAL BUILDING
 @ B.V.NAGAR

SALB AREA:
 14.31 ANK

DRAWN BY:

AKASH
 DATE: 10-02-2026


CONSULTANTS:



SYAM INFRA

1-3-99, Bangalathota, Nawabpet,
 Nellore-524002

PH. No. : 9849525991, 9440277610
 E.MAIL : syaminfra@gmail.com

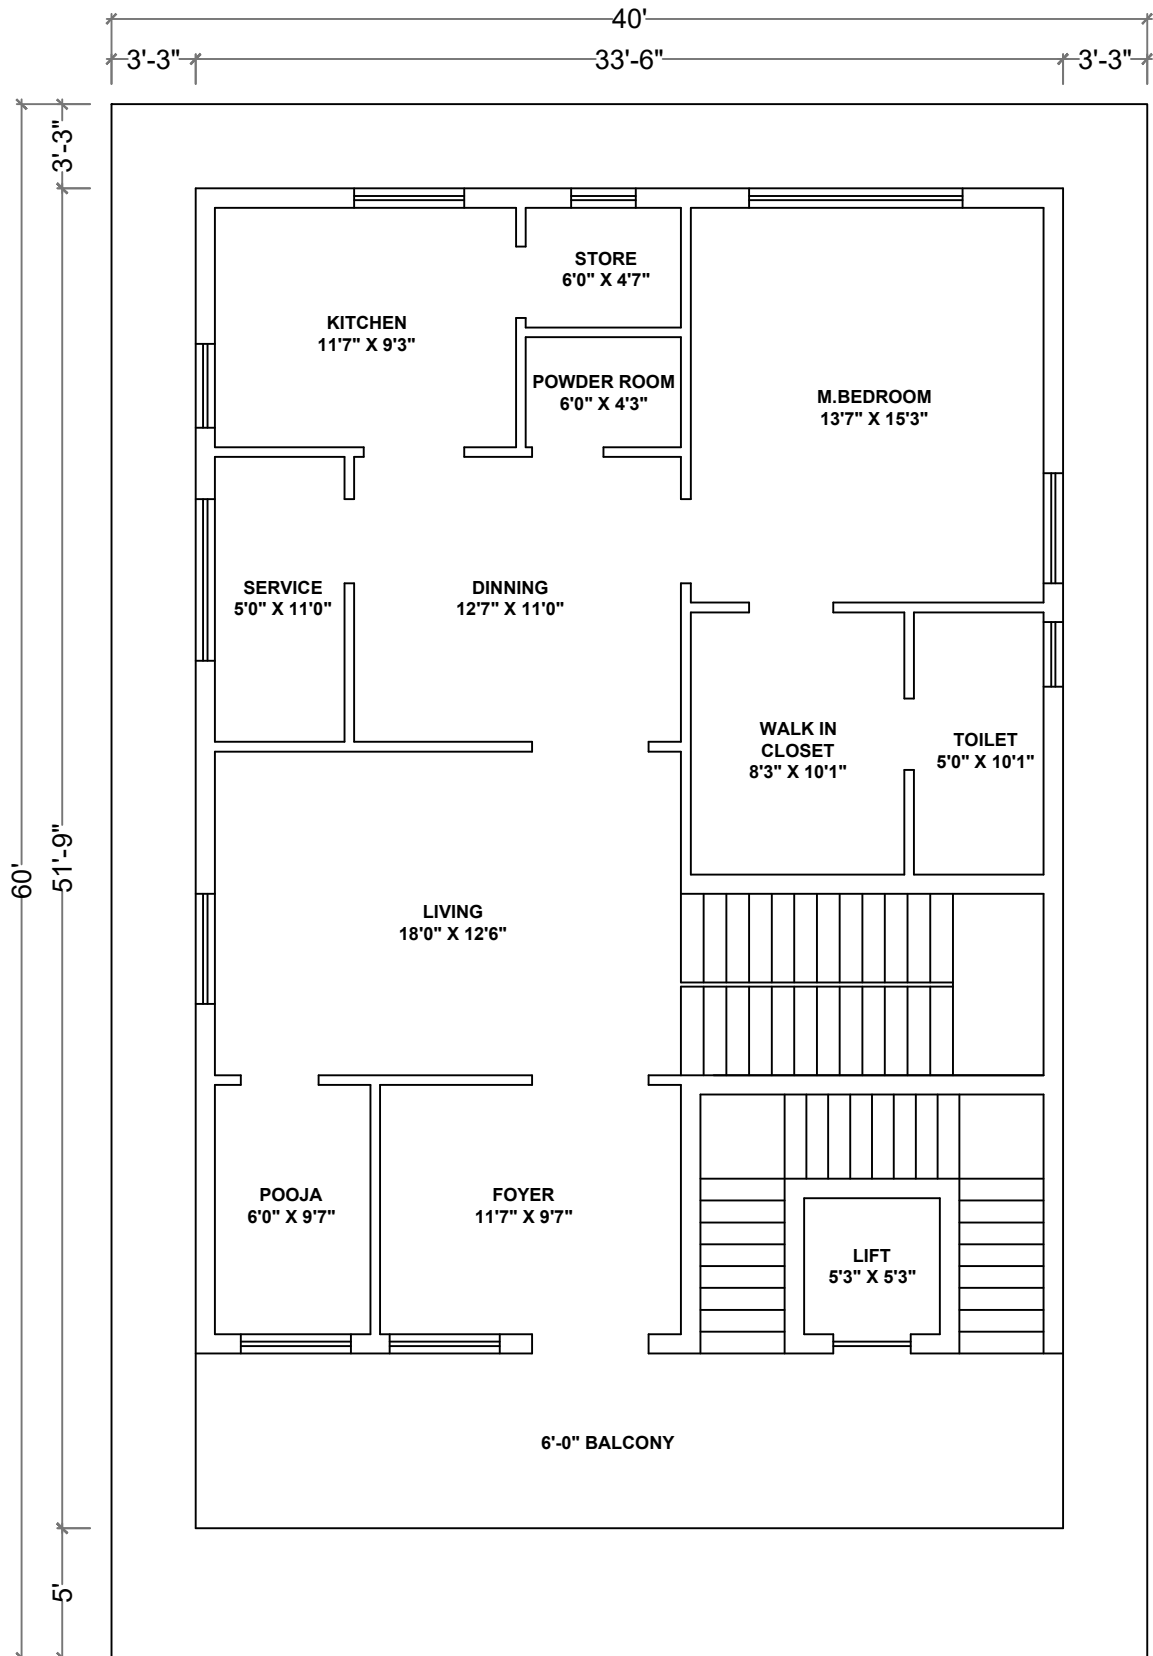

NOTES:

1. ALL THE DIMENSIONS MENTIONED ARE IN FEET & INCHES.
2. DRAWINGS NOT TO BE SCALED ONLY WRITTEN DIMENSIONS TO BE FOLLOWED.
3. ANY DISCREPANCIES FOUND IN THE DRAWING SHALL BE BROUGHT TO THE NOTICE OF THE CONSULTANT BEFORE EXECUTION.
4. RELEVANT SERVICES DRAWING TO BE READ SIMULTANEOUSLY.
5. FINISHED FLOOR TO BE 100MM FROM UNFINISHED FLOOR LEVELS.

ORIENTATION:



CLIENT NAME:

SRI.D.VENKATA RAO

CHECKED BY: SYAM

APPROVED BY: SESA REDDY

DRAWN BY:

AKASH

DATE: 10-02-2026

TITLE:

FIRST FLOOR PLAN -1

PROJECT NAME:

RESIDENTIAL BUILDING @ B.V.NAGAR

SALB AREA:

14.31 ANK

CONSULTANTS:




SYAM INFRA

1-3-99, Bangalathota, Nawabpet,
Nellore-524002

PH. No. : 9849525991, 9440277610

E.MAIL : syaminfra@gmail.com

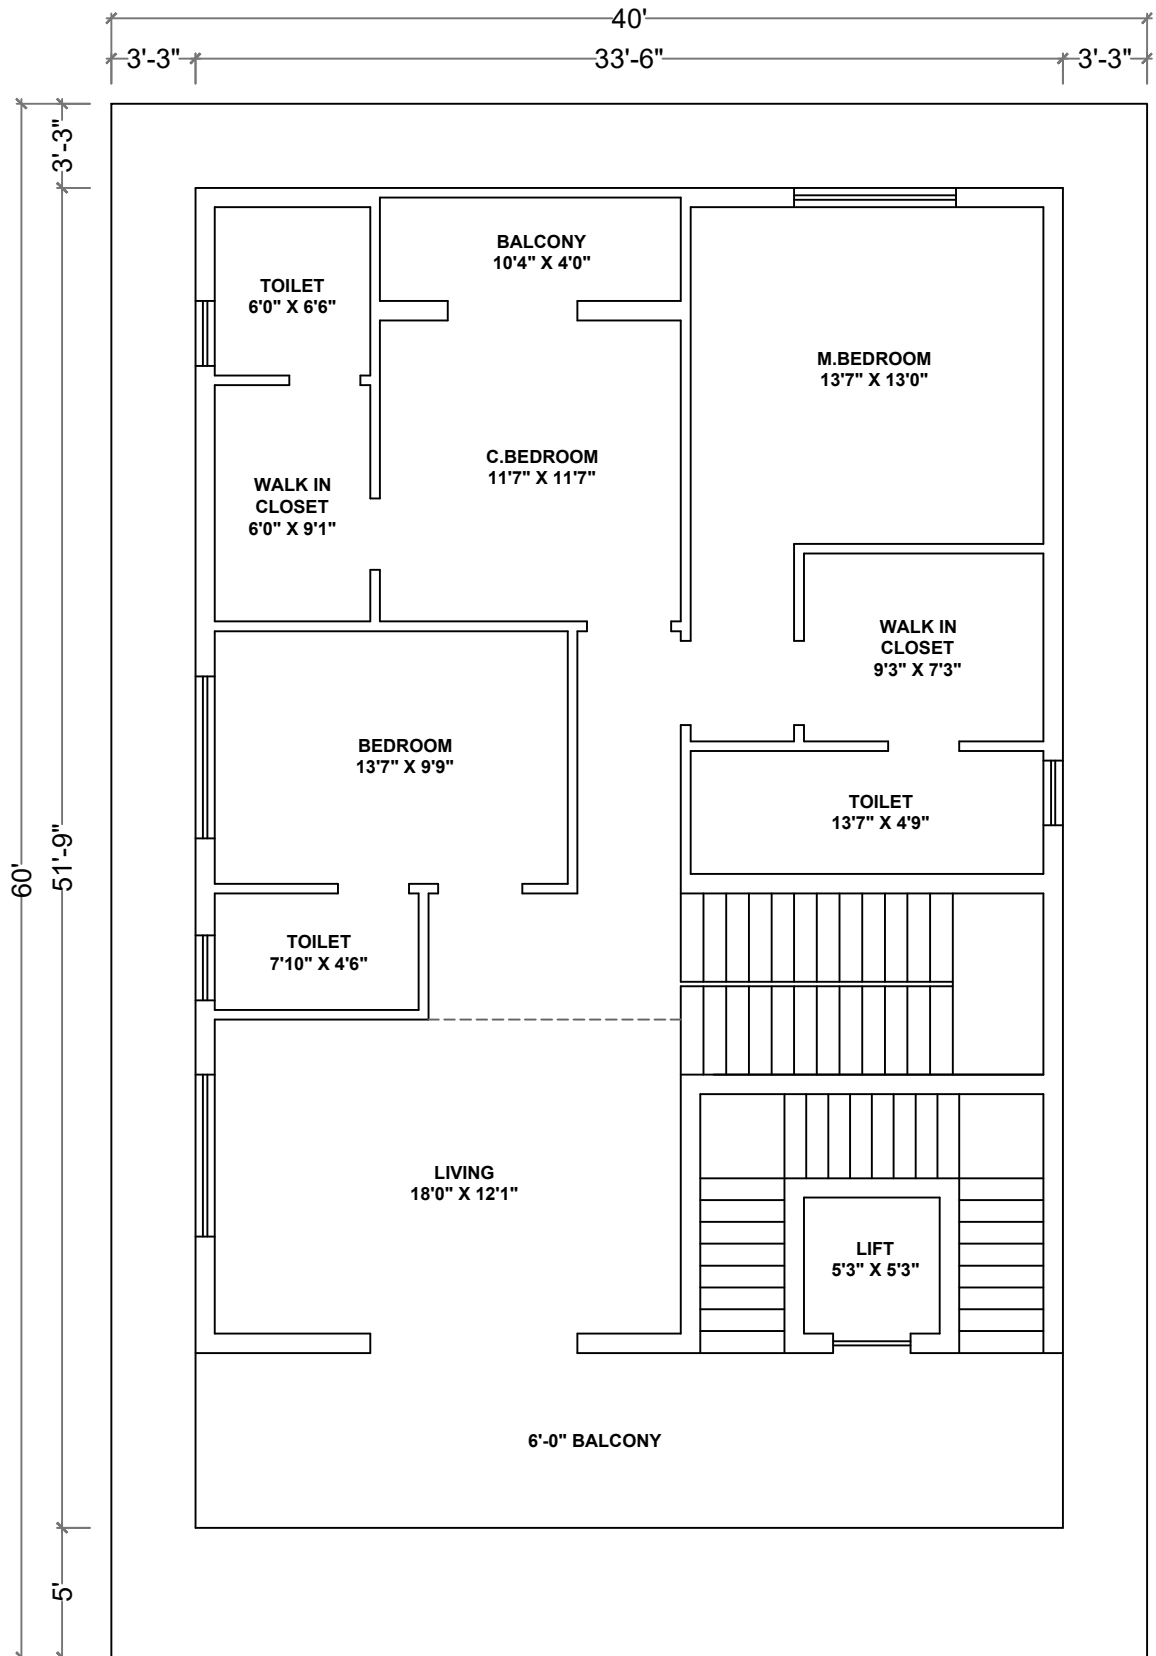

NOTES:

1. ALL THE DIMENSIONS MENTIONED ARE IN FEET & INCHES.
2. DRAWINGS NOT TO BE SCALED ONLY WRITTEN DIMENSIONS TO BE FOLLOWED.
3. ANY DISCREPANCIES FOUND IN THE DRAWING SHALL BE BROUGHT TO THE NOTICE OF THE CONSULTANT BEFORE EXECUTION.
4. RELEVANT SERVICES DRAWING TO BE READ SIMULTANEOUSLY.
5. FINISHED FLOOR TO BE 100MM FROM UNFINISHED FLOOR LEVELS.

ORIENTATION:



CLIENT NAME:

SRI.D.VENKATA RAO

CHECKED BY:

SYAM

APPROVED BY:

SESHA REDDY

DRAWN BY:

AKASH

DATE:

10-02-2026

TITLE:

SECOND FLOOR PLAN -1

PROJECT NAME:

RESIDENTIAL BUILDING
@ B.V.NAGAR

SALB AREA:

14.31 ANK

CONSULTANTS:



SYAM INFRA

1-3-99, Bangalathota, Nawabpet,
Nellore-524002

PH. No. : 9849525991, 9440277610

E.MAIL : syaminfra@gmail.com